




CROQUIS DE UBICACION

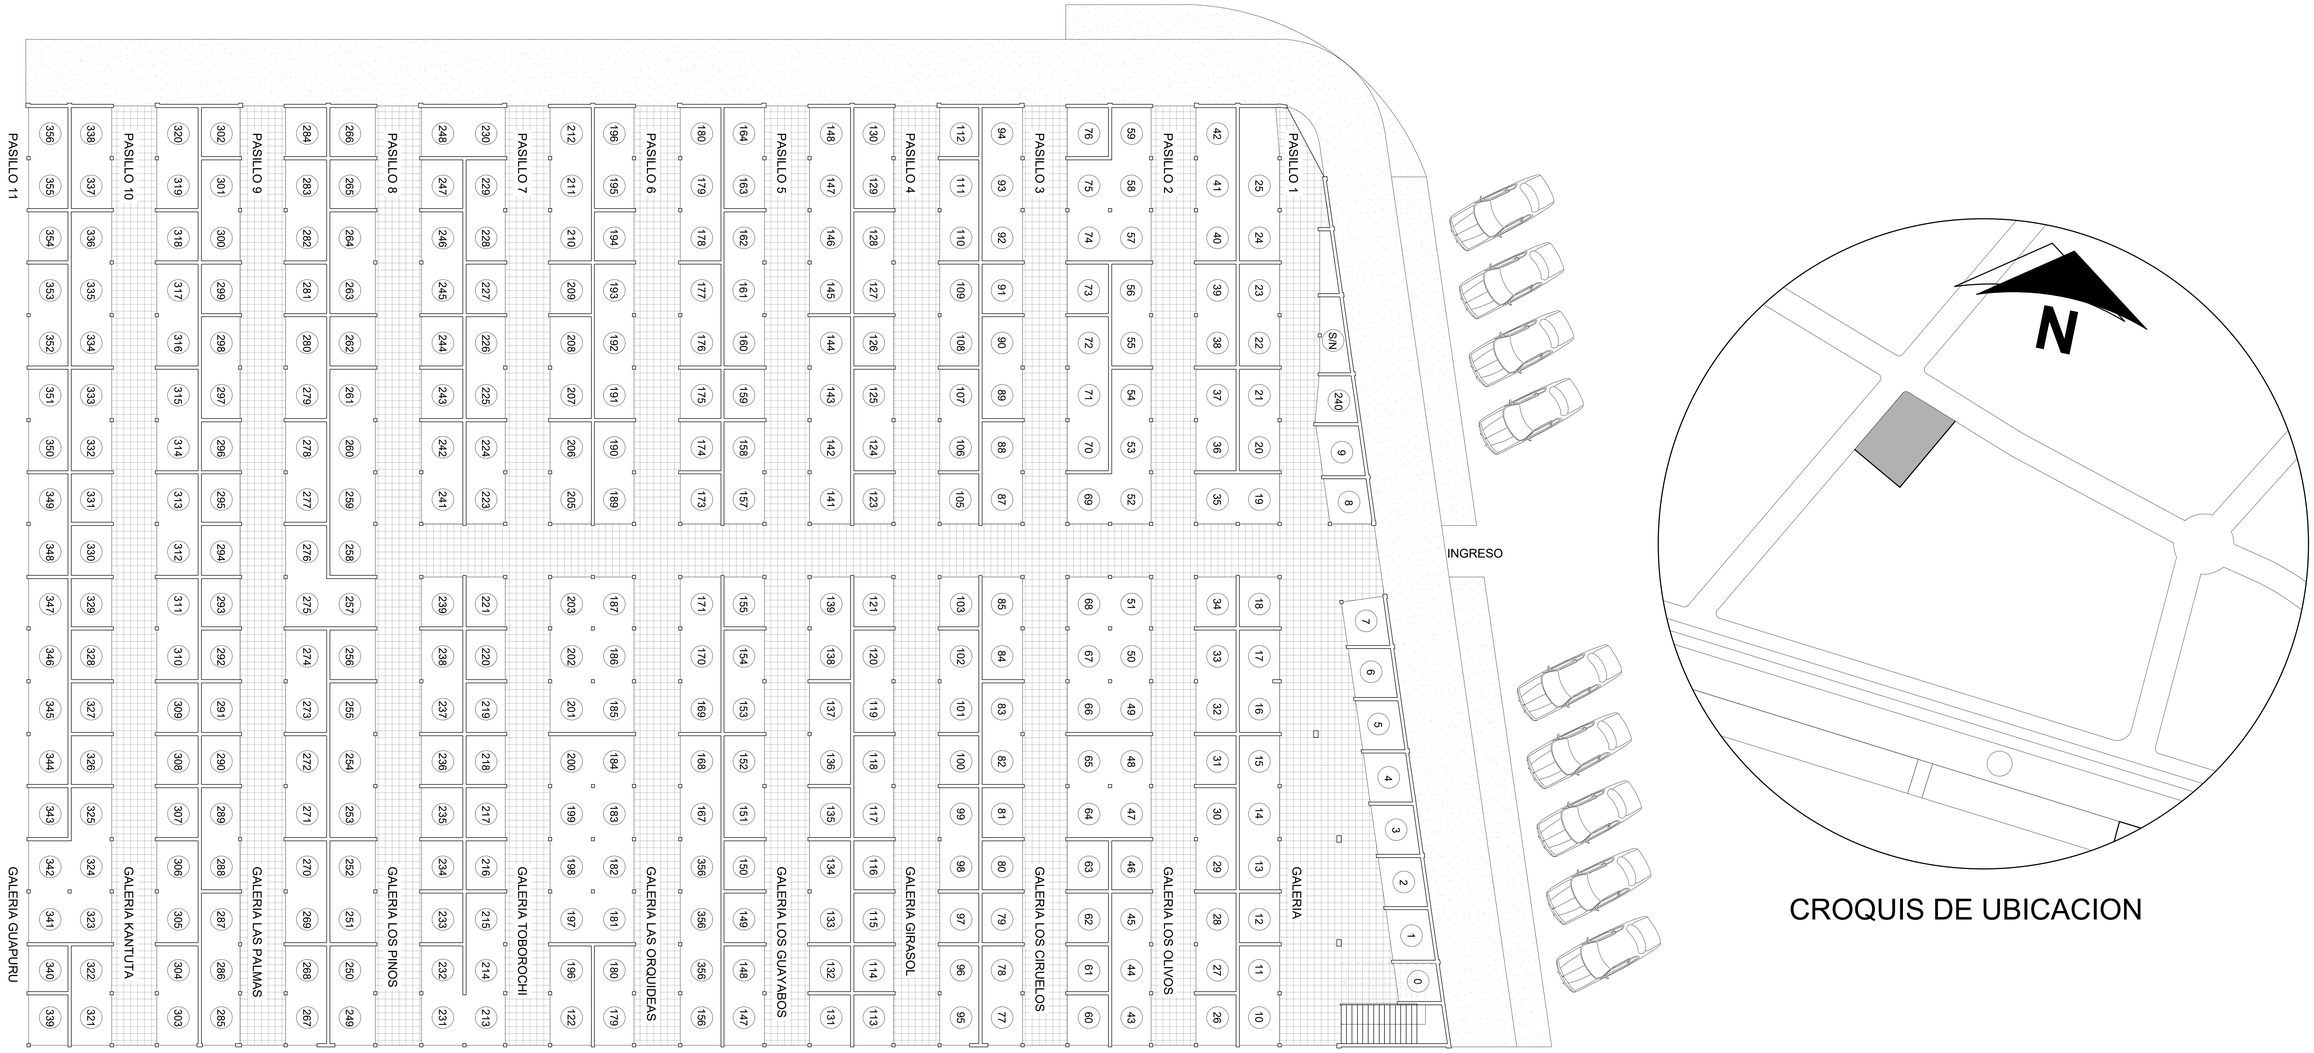

FACHADA PRINCIPAL

PROYECTO:	ASOCIACION 13 DE JULIO
UBICACION:	FERIA BARRIO LINDO
PLANO:	PLANTA BAJA ARQUITECTONICA
ESCALA:	1:100
FECHA:	09/2021
SUP. DE TERRENO	3272.76 M2
SUP. DE CONSTRUCCION:	2710.76 M2
ACOTACION:	METROS

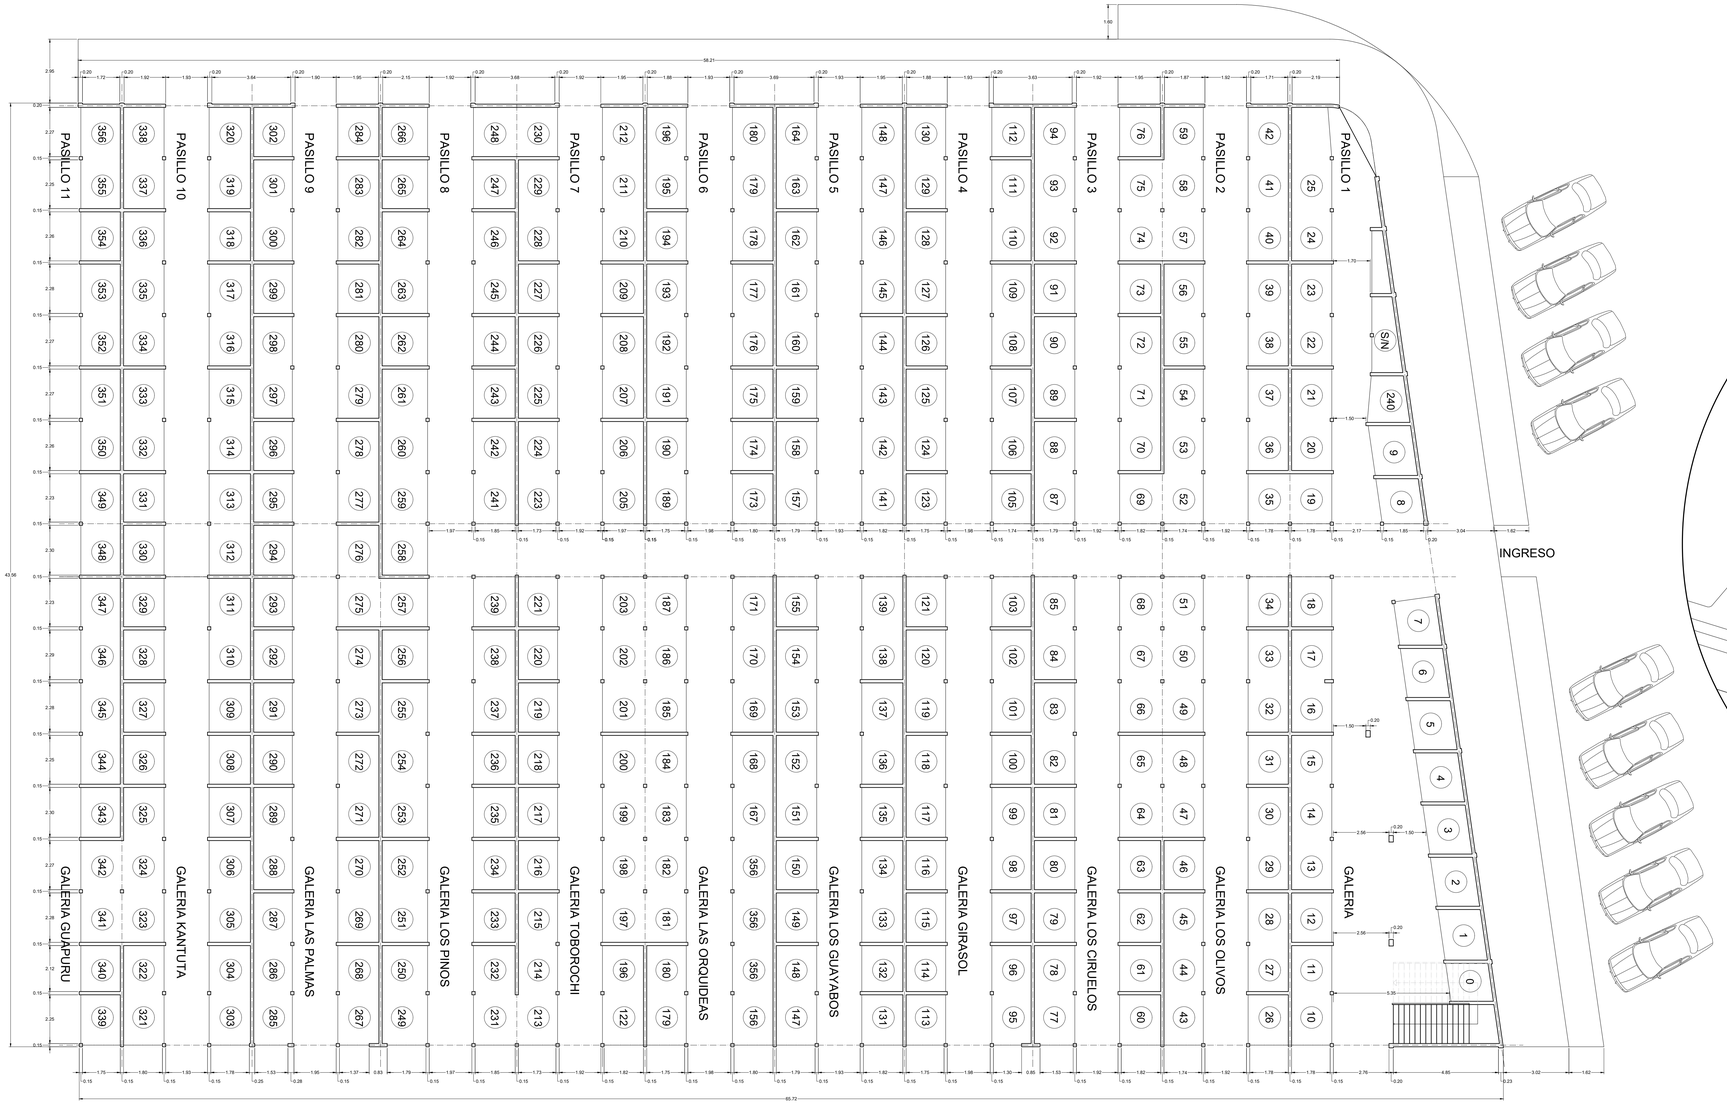

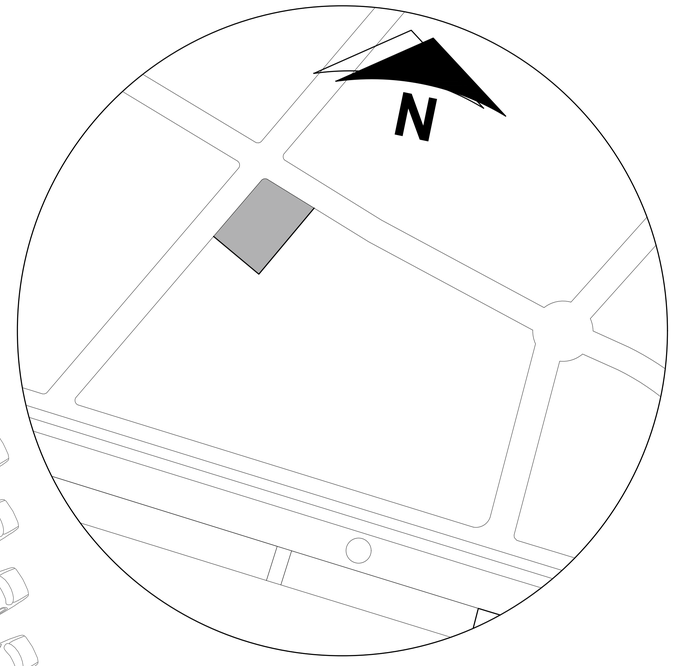



CROQUIS DE UBICACION



FACHADA PRINCIPAL

PROYECTO: ASOCIACION 13 DE JULIO			
UBICACION: FERIA BARRIO LINDO			
PLANO: PLANTA BAJA TECNICA			
		ESCALA: 1:100	FECHA: 09/2021
	SUP. DE TERRENO 3272.76 M2	SUP. DE CONSTRUCCION: 2710.76 M2	ACOTACION: METROS

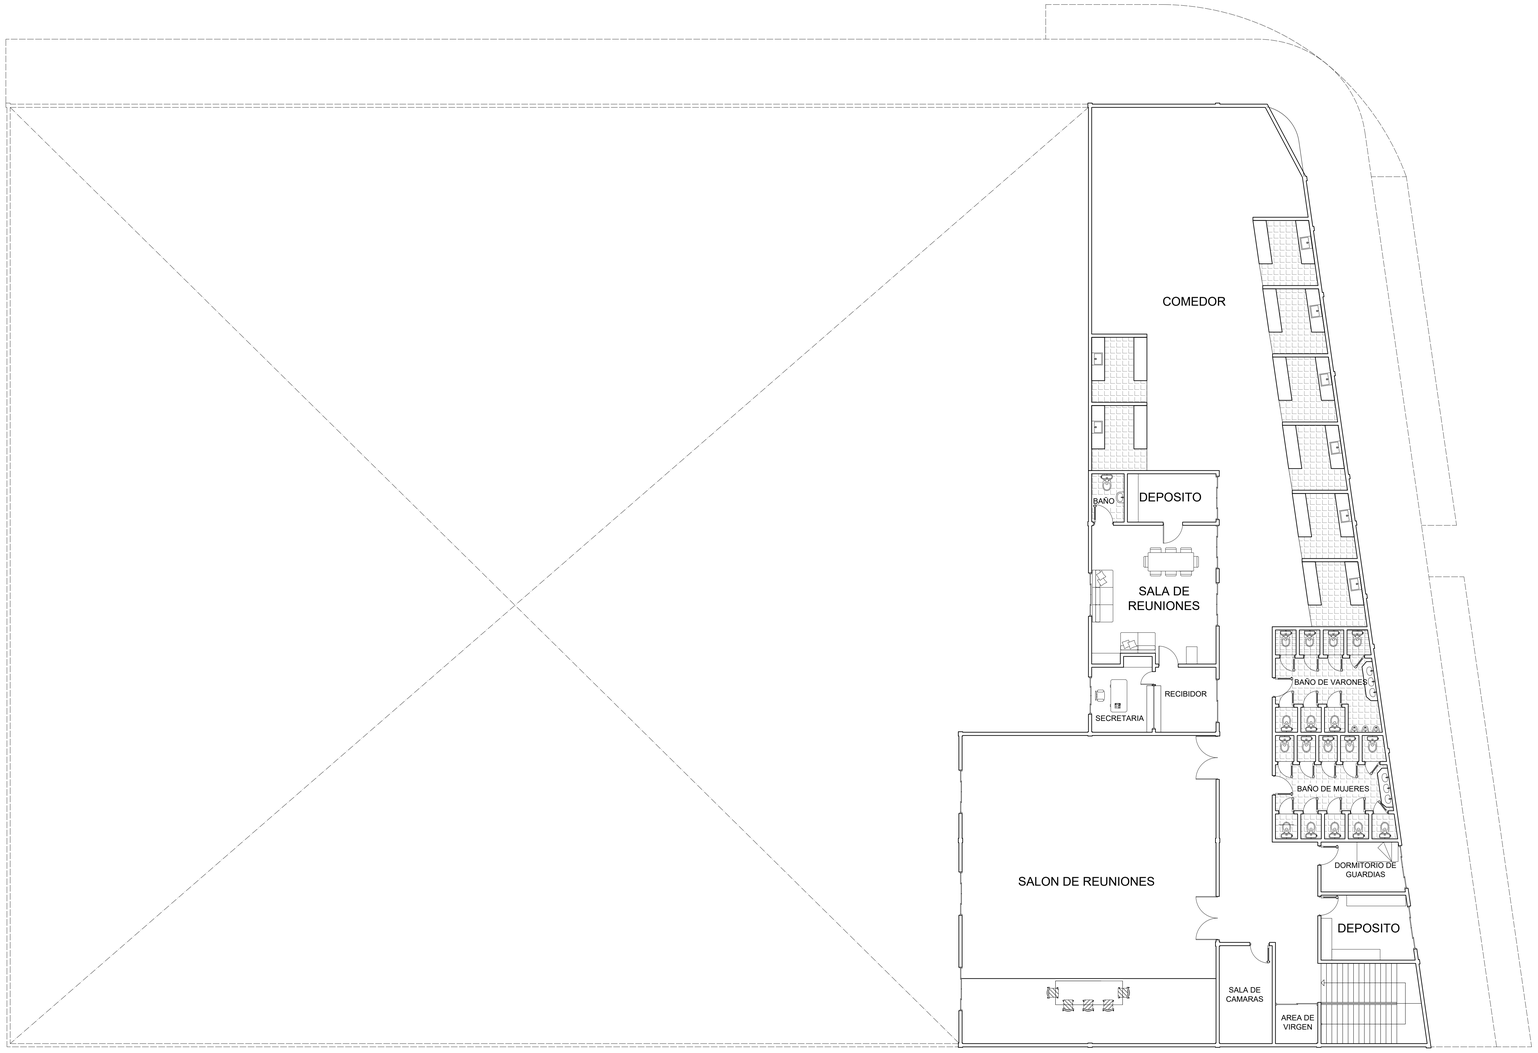

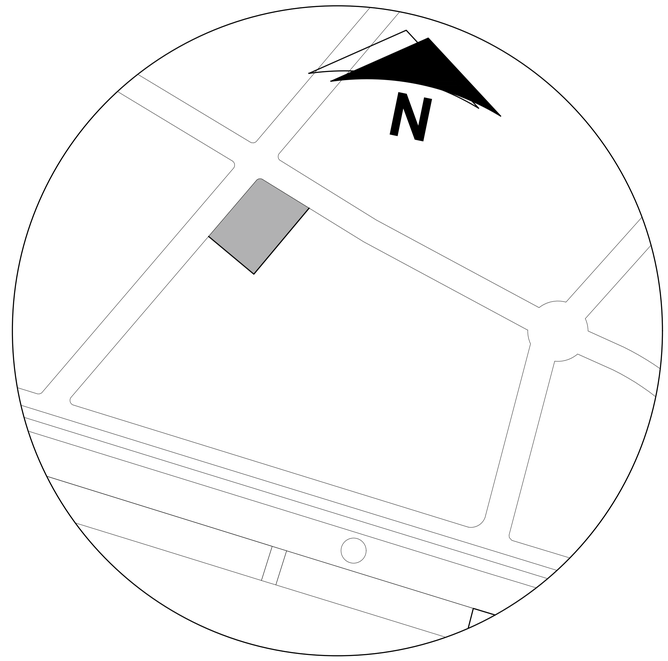

CROQUIS DE UBICACION



FACHADA PRINCIPAL

PROYECTO: ASOCIACION 13 DE JULIO

UBICACION: FERIA BARRIO LINDO

PLANO: PLANTA ALTA ARQUITECTONICA


ESCALA: 1:100


FECHA: 09/2021

SUP. DE TERRENO 3272.76 M2

SUP. DE CONSTRUCCION: 2710.76 M2

ACOTACION: METROS

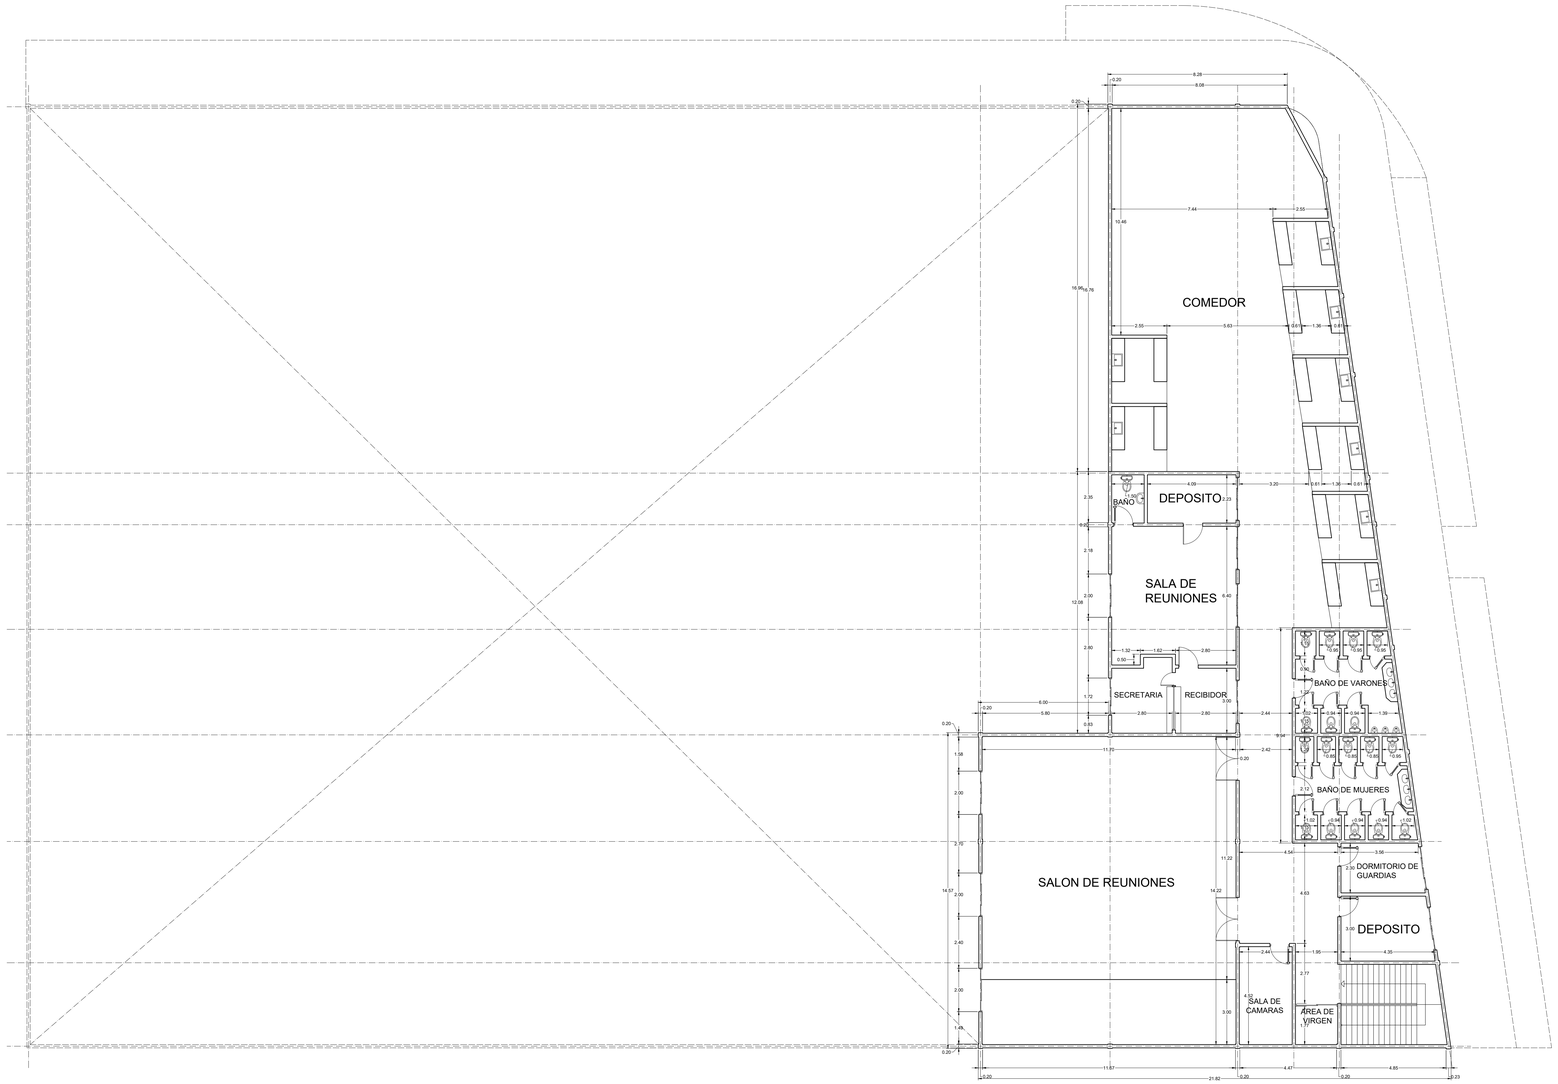

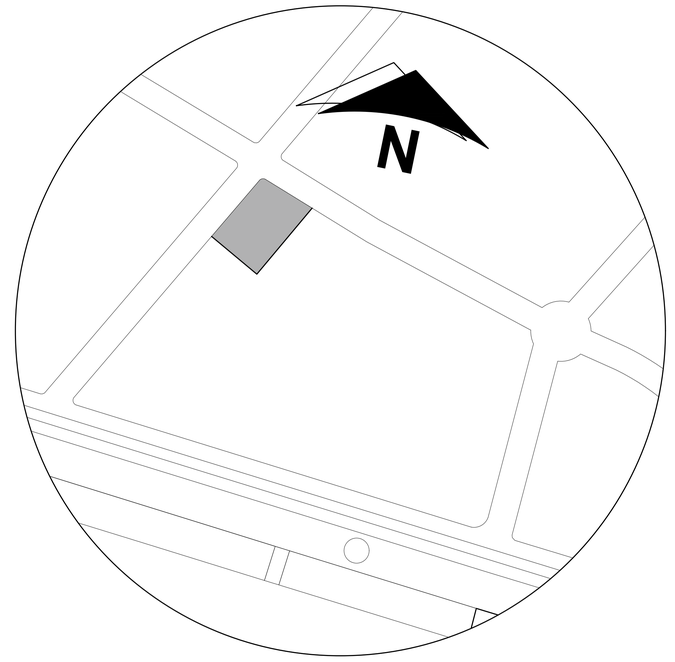

CROQUIS DE UBICACION



FACHADA PRINCIPAL

PROYECTO: ASOCIACION 13 DE JULIO

UBICACION: FERIA BARRIO LINDO

PLANO: PLANTA ALTA TECNICA


ESCALA: 1:100


FECHA: 09/2021

SUP. DE TERRENO 3272.76 M2

SUP. DE CONSTRUCCION: 2710.76 M2

ACOTACION: METROS

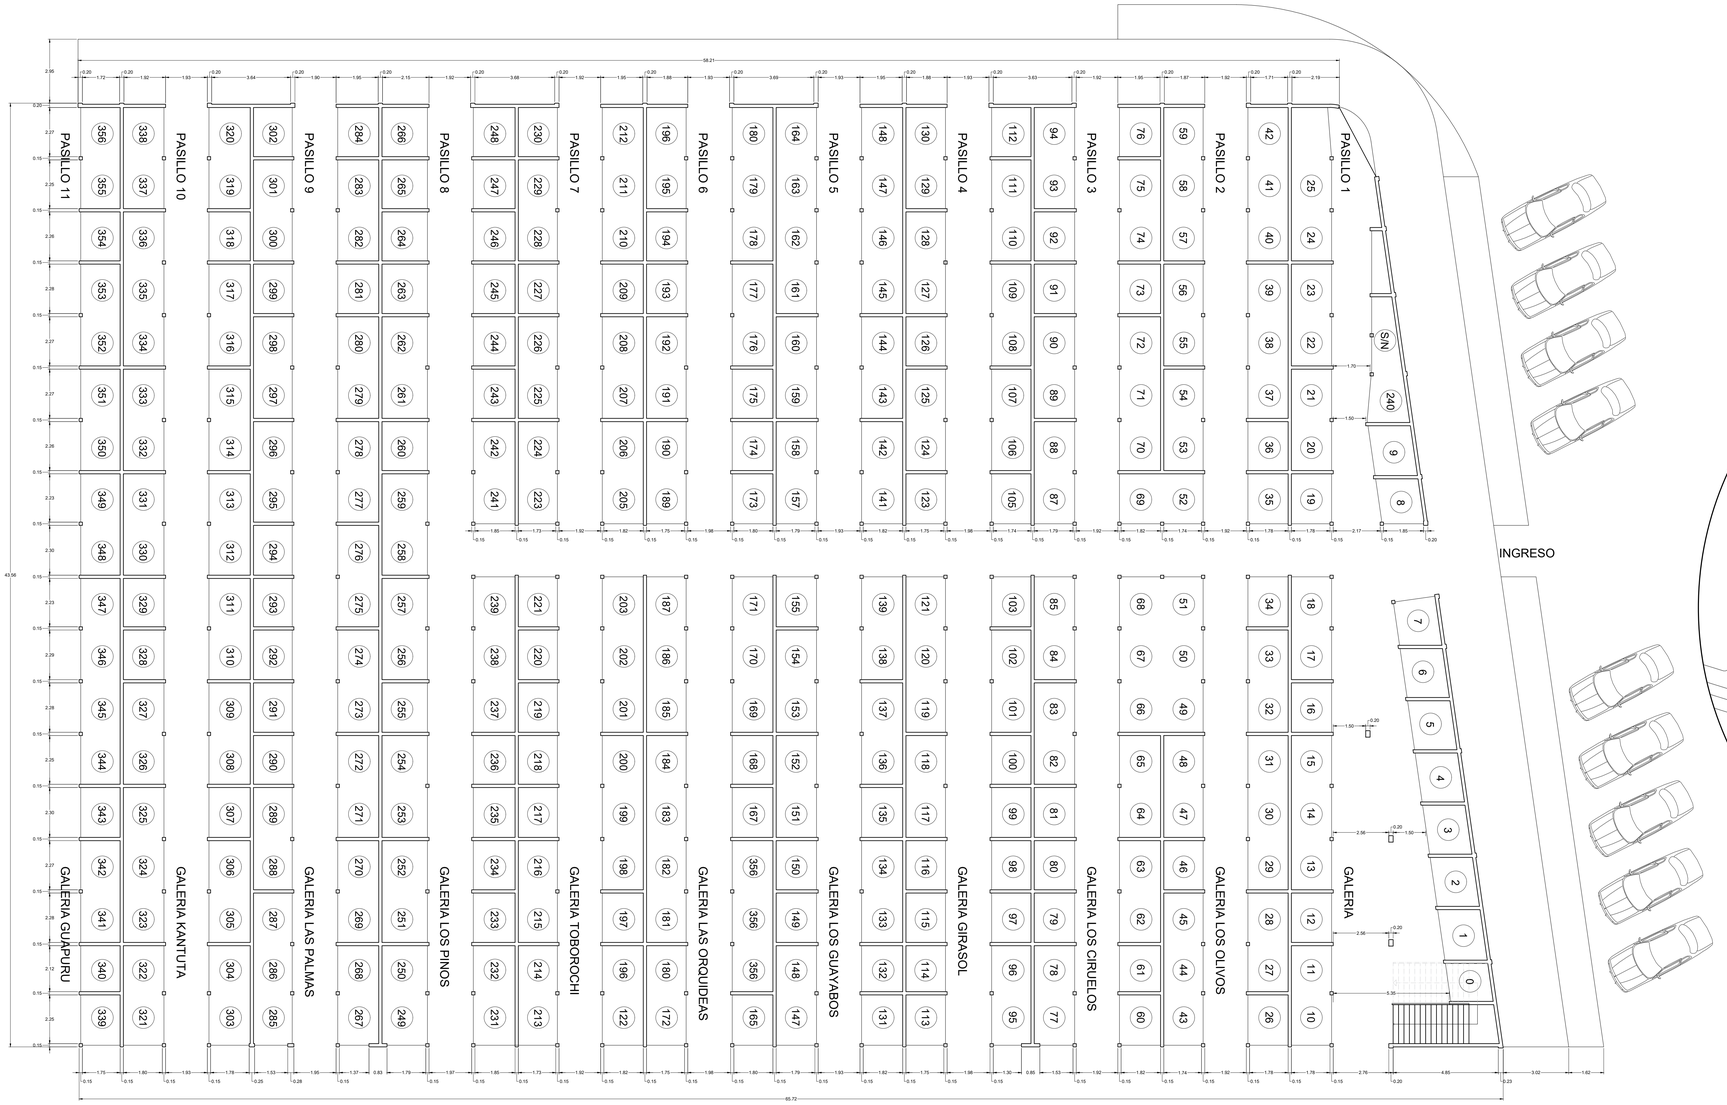

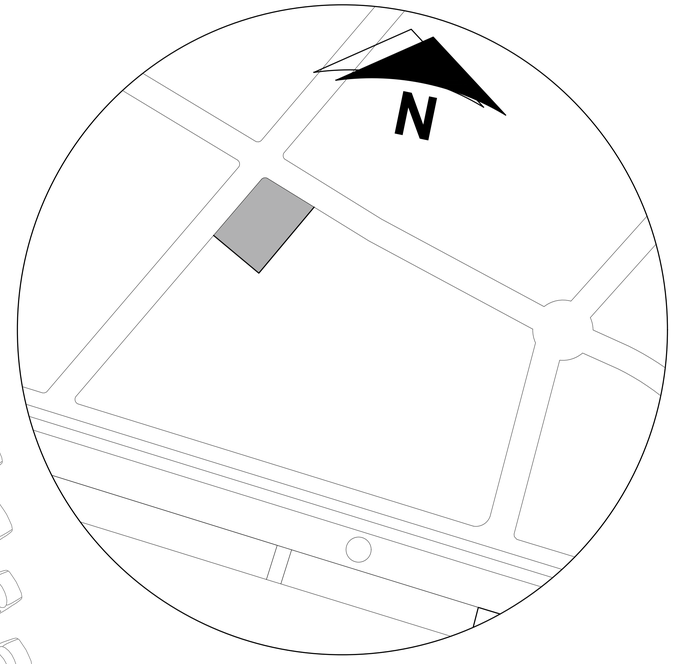

CROQUIS DE UBICACION



FACHADA PRINCIPAL

PROYECTO:	ASOCIACION 13 DE JULIO
UBICACION:	FERIA BARRIO LINDO
PLANO:	PLANTA BAJA - 2017
ESCALA:	1:100
FECHA:	09/2021
SUP. DE TERRENO	3272.76 M2
SUP. DE CONSTRUCCION:	2710.76 M2
ACOTACION:	METROS